

PROJECT NO. 506-26-201 ROOF REPLACEMENT, B1W

VA ANN ARBOR HEALTHCARE SYSTEM

DEPARTMENT OF VETERANS AFFAIRS

ANN ARBOR, MICHIGAN

100% BID DOCUMENTS

PROJECT TEAM


LOCATION MAP

OWNER:
OFFICE OF CONSTRUCTION &
FACILITES MANAGEMENT
DEPARTMENT OF VETERANS AFFAIRS
2215 FULLER ROAD
ANN ARBOR, MI, 48105

ARCHITECTURE:
ALLIANCE | 7GAE JV
600 E. MICHIGAN AVENUE - SUITE B
KALAMAZOO, MI 49007
PHONE: 269.927.0144
FAX: 269.593.5933
WEB: WWW.7GENAE.COM



ANN ARBOR, MICHIGAN

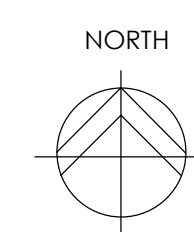

SHEET	DESCRIPTION	ISSUE DATE
G001	COVER SHEET	DECEMBER 1, 2023
GS100	SITE CAMPUS MAP	DECEMBER 1, 2023
01W-AS140	COMPOSITE ROOF PLAN	DECEMBER 1, 2023
01W-AS141	ROOF PLAN - UNIT A	DECEMBER 1, 2023
01W-AS200	EXTERIOR ELEVATIONS	DECEMBER 1, 2023
01W-AS201	EXTERIOR ELEVATIONS	DECEMBER 1, 2023
01W-AS340	ROOF SECTIONS AND DETAILS	DECEMBER 1, 2023


PROJECT #506-21-202	SIGNATURE	DATE
DIRECTOR		
ASSOCIATE DIRECTOR		
CHIEF OF STAFF		
CHIEF, PMO		
CHIEF, ENGINEERING SECTION		
CHIEF, ENVIRONMENTAL MANAGEMENT SECTION		
INFECTION CONTROL OFFICER		
PATIENT SAFETY MANAGER		
GENS COORDINATOR		
SAFETY SPECIALIST		
CHIEF, POLICE SERVICE		
CHIEF, FIRE SERVICE		
UNION SAFETY REPRESENTATIVE		
CONTRACTING OFFICER		
COB		
ASSOCIATE DIRECTOR FOR PATIENT CARE SERVICES		

		CONSULTANT	ARCHITECT/ENGINEER OF RECORD	STAMP	Office of Construction and Facilities Management	Drawing Title COVER SHEET	Phase 100% BID DOCUMENTS	Project Title ROOF REPLACEMENT	Project Number 220109
						Approved: PROJECT DIRECTOR	Sprinkler:	Location ANN ARBOR VAMC	Building Number 1W
								Issue Date DECEMBER 1, 2023	Checked JD
								Drawn GN	Drawing Number G001
									DWG. 01 OF 08


SITE CAMPUS MAP LEGEND

BUILDING ROOF IN SCOPE OF WORK


PROPOSED PROJECT LAYDOWN AREAS (TO BE
CONFIRMED BY CONTRACTOR W/ COR)

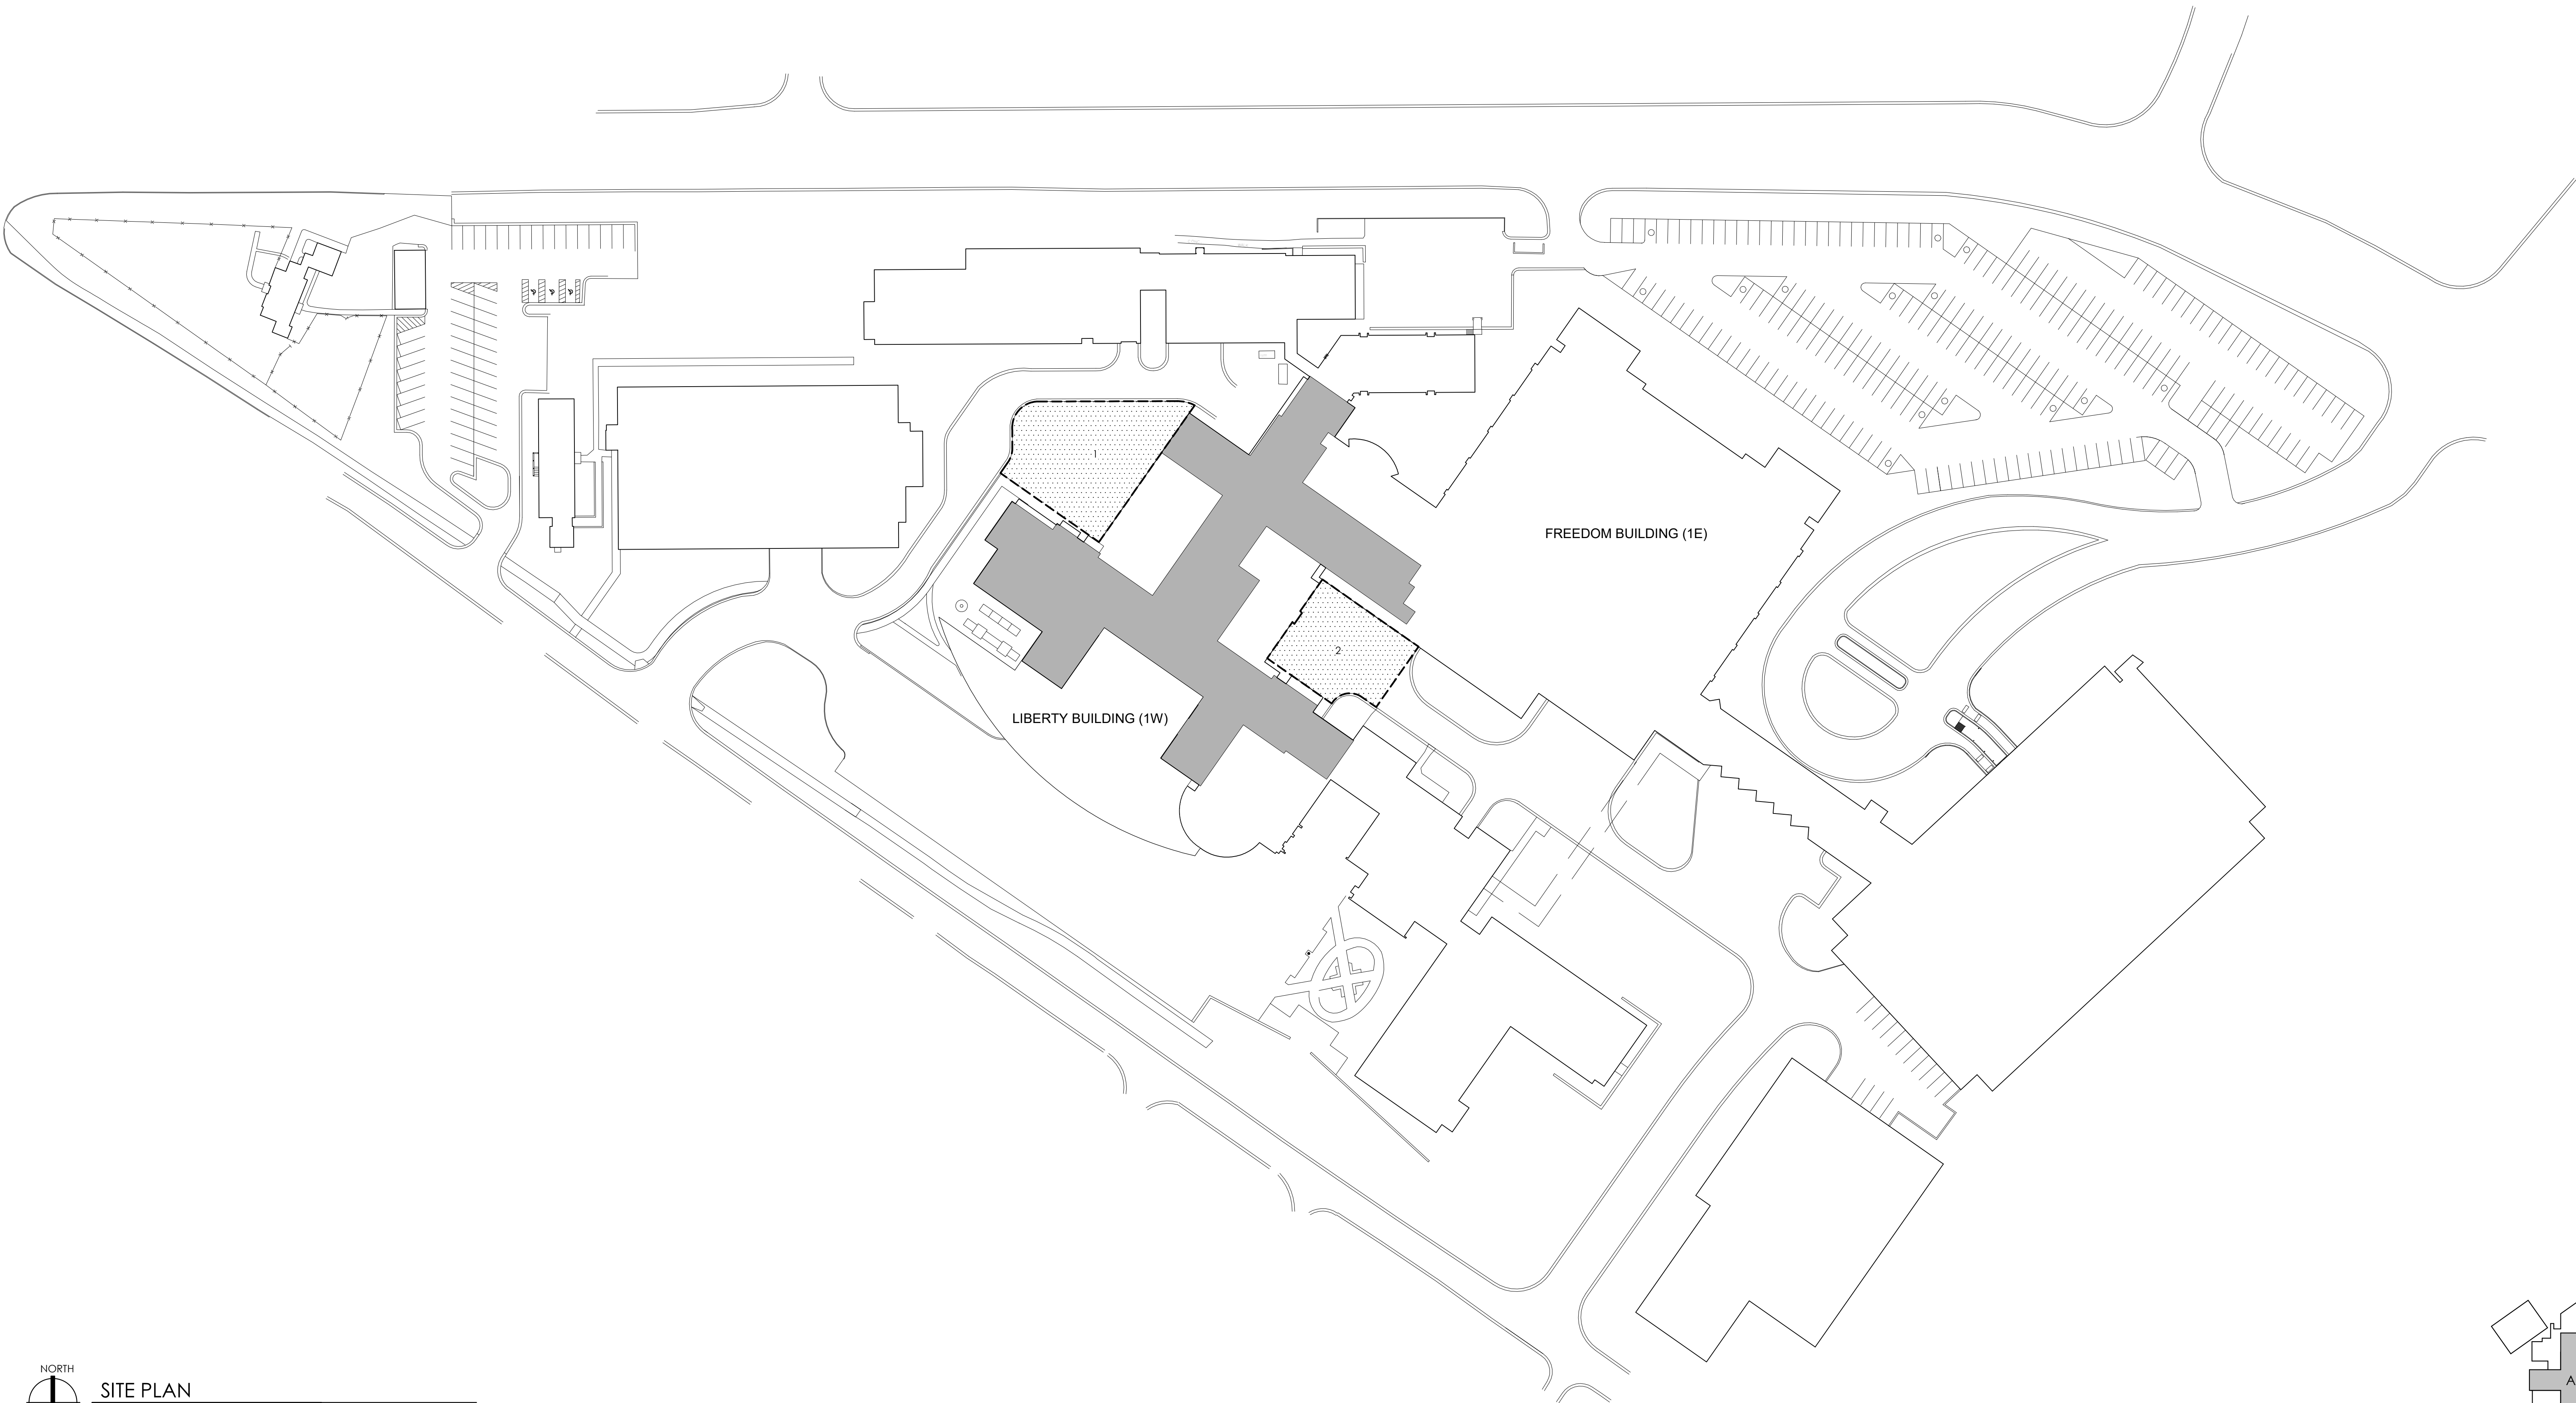


NORTH
SITE PLAN
SCALE: 1" = 60'-0"

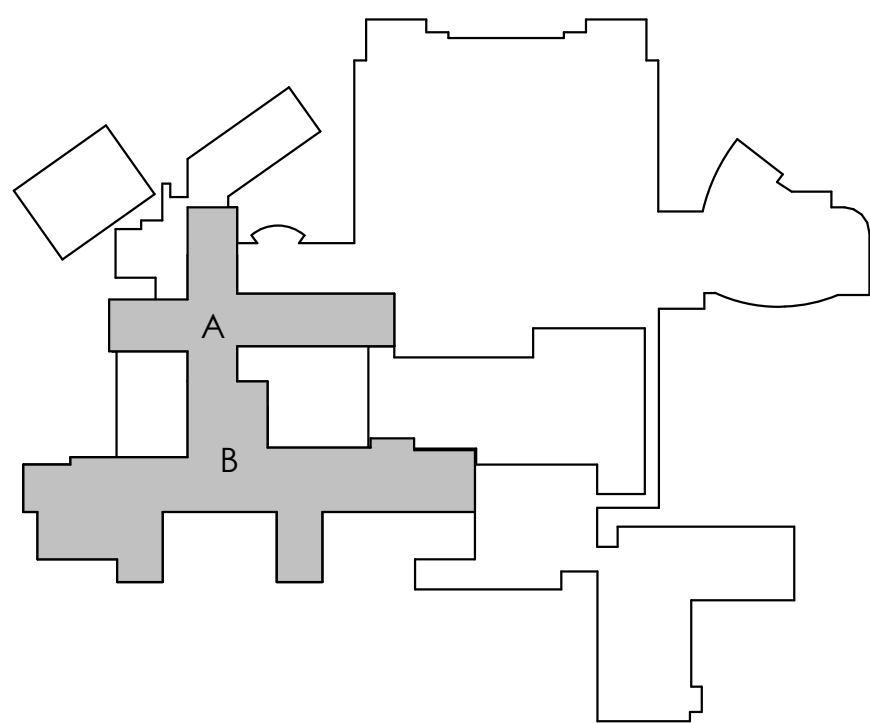


		CONSULTANT	ARCHITECT/ENGINEER OF RECORD		STAMP	Office of Construction and Facilities Management	Drawing Title SITE CAMPUS MAP	Phase 100% BID DOCUMENTS	Project Title ROOF REPLACEMENT	Project Number 220109						
100% BID DOCUMENTS		12/01/23		Alliance Consulting Group		U.S. Department of Veterans Affairs	Approved: PROJECT DIRECTOR	Sprinkler:	Location ANN ARBOR VAMC	Drawing Number GS100						
Revisions:		Date:		Joint Venture												

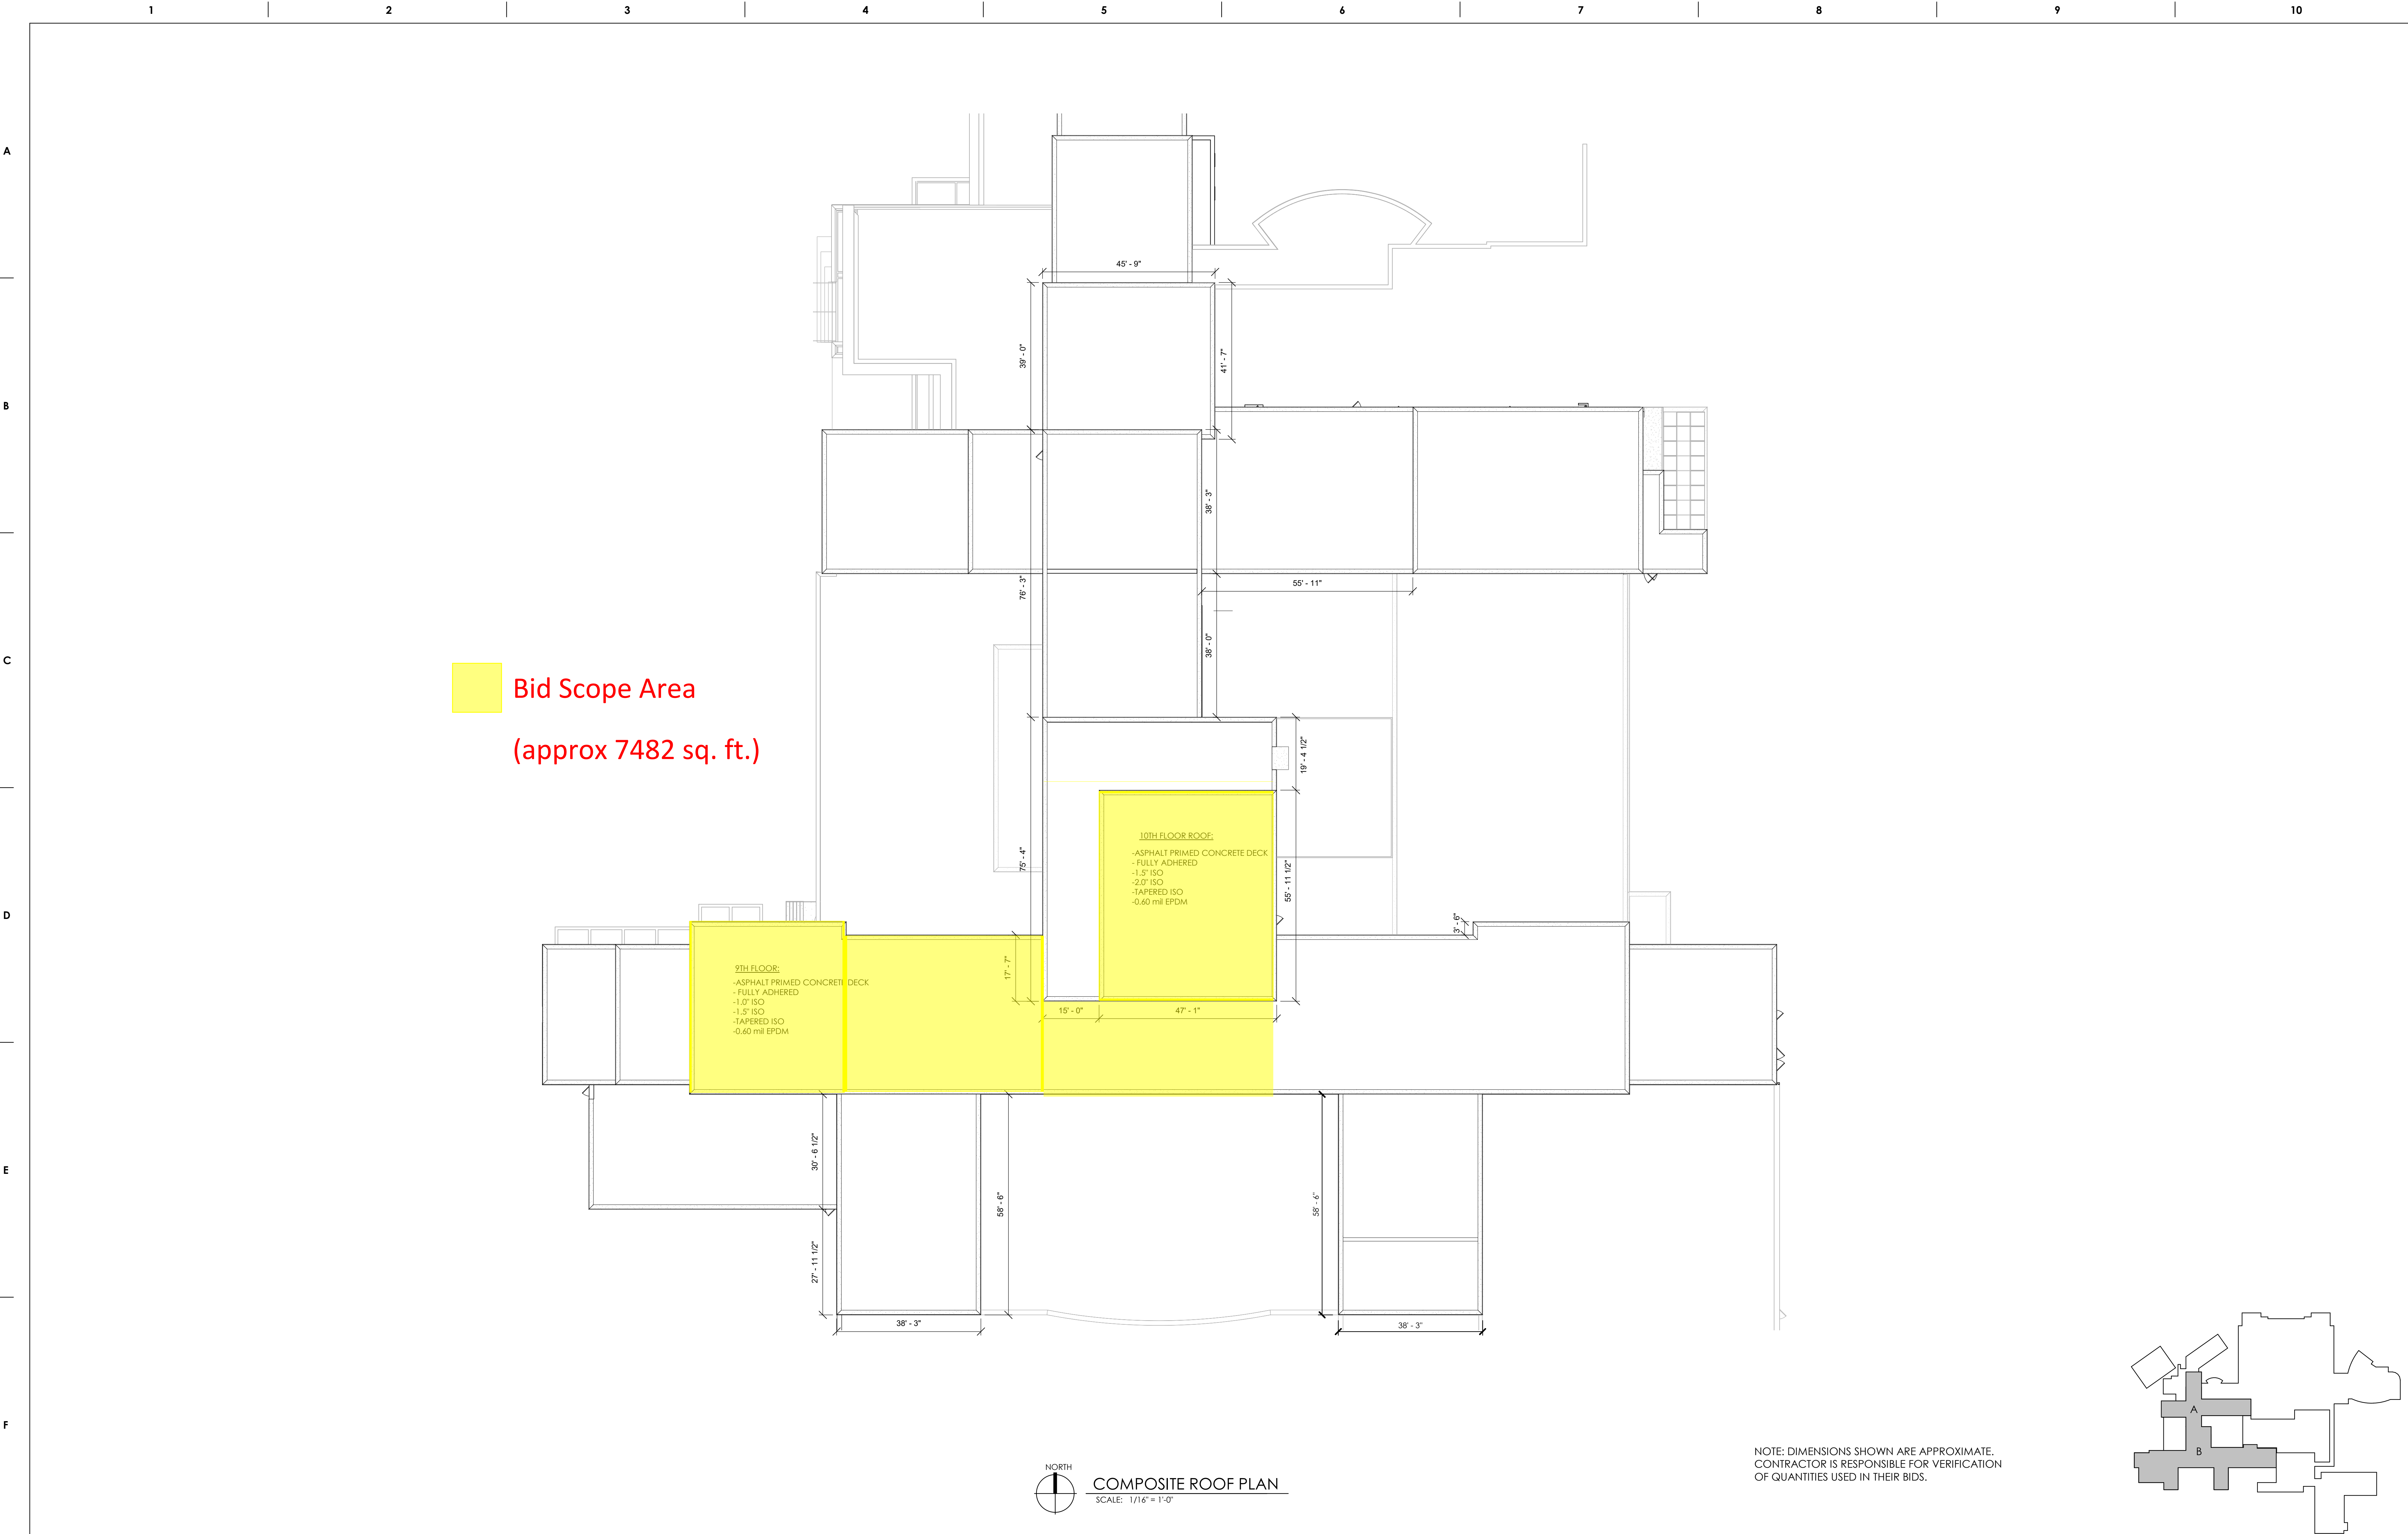

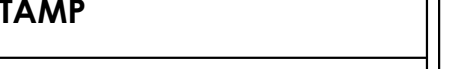		CONSULTANT	ARCHITECT/ENGINEER OF RECORD	STAMP  Office of Construction and Facilities Management VA U.S. Department of Veterans Affairs	Drawing Title COMPOSITE ROOF PLAN	Phase 100% BID DOCUMENTS	Project Title ROOF REPLACEMENT	Project Number 220109	
									Building Number 1W
					Approved: PROJECT DIRECTOR	Sprinkler:	Location ANN ARBOR VAMC	Drawing Number 01W-AS140	
100% BID DOCUMENTS	12/01/23								
Revisions:	Date:								


DEMOLITION KEYNOTES	
1 REMOVE EXISTING (LOW SLOPE) BUILT-UP, ROLLED OR EPDM ROOFING AND INSULATION LAYERS DOWN TO THE DECK - COMPLETE TEAR-OFF INCLUDING ALL FASTENERS. PREP FOR NEW ROOF SYSTEM AS INDICATED. ALTERNATE 1: EXISTING INSULATION TO REMAIN.	6 EXISTING VENTS, DRAINS, EQUIPMENT OR OTHER ROOFTOP PENETRATIONS TO REMAIN. U.N.O. REMOVE ANY PIPE ROOTS, FLASHING, AND SEALANTS AROUND PENETRATIONS. RAISE TO RECEIVE NEW ROOFING AND INSULATION SYSTEM. EXISTING ROOF DRAIN PIPING TO REMAIN FOR RECONNECTION. REMOVE AND REPLACE EXISTING DRAIN BODY, SUMP AND ASSOCIATED FASTENERS. COMPLETELY REMOVE ANY DEBRIS FROM EXISTING ROOF DRAIN PIPE TO ALLOW FOR PROPER DRAINAGE.
2 REMOVE EXISTING METAL FASCIA/COPING AND REPLACE WITH NEW AS SHOWN/SPECIFIED.	7 PREVIOUS EXISTING ROOF VENT (OR OTHER) LOCATION. PATCH/INFILL WITH NEW ROOF DECK MATERIAL AND SHIM AS REQUIRED TO BE FLUSH WITH ADJACENT EXISTING. ENSURE PATCHES ARE ADEQUATELY SUPPORTED TO MEET CODE MIN. LIVE AND DEAD LOAD DESIGN CRITERIA. ALL WORK TO BE COMPLETED FROM ABOVE. FILL ANY GAPS IN THE INSULATION BARRIER WITH LIKE MATERIALS MATCHING QUALITY AND PERFORMANCE. AT OPENINGS LARGER THAN 6 INCH DIAMETER, RETAIN EXISTING CURB STRUCTURE. FRAME ACROSS OPENING WITH P.T. 2X6 AT 16" O.C. WITH 3/4" MARINE GRADE PLYWOOD DECK. INSTALL INSULATION, COVERBOARD AND EPDM OVER NEW ASSEMBLY.
3 EXISTING INTERNAL ROOF DRAIN TO REMAIN. MODIFY/ADJUST HEIGHT AND ADD COLLAR EXTENSION AS NEEDED TO ACCOMMODATE NEW ROOF INSULATION THICKNESS.	8 CAPPED PIPES. REMOVE AND CAP BELOW ROOF-LINE. ALL WORK TO BE COMPLETED FROM ABOVE.
4 REMOVE EXISTING LIGHTNING PROTECTION COMPONENTS FOR ROOF REPLACEMENT WORK. EXISTING AIR TERMINALS CAN BE REUSED AS LONG AS THEIR PHYSICAL CONDITION IS INTACT, EXISTING DOWNSLEADS AND GROUNDING ARE MOSTLY INTACT AND CAN BE REUSED WITH MINOR REPAIRS, REATTACHMENT AND RE-ROUTE AS REQUIRED TO MEET PERFORMANCE SPEC REQUIREMENTS FOR A COMPLETE AND FUNCTIONAL SYSTEM.	NOTE: ALL KEY NOTES FOR THE PROJECT ARE LISTED BUT DO NOT NECESSARILY APPLY TO EVERY PLAN OR ELEVATION. REFER TO DRAWINGS FOR APPLICABILITY. SEE SPECIFICATIONS FOR GENERAL DEMOLITION AND PATCHING REQUIREMENTS.
5 REMOVE EXISTING ROOFTOP EQUIPMENT.	

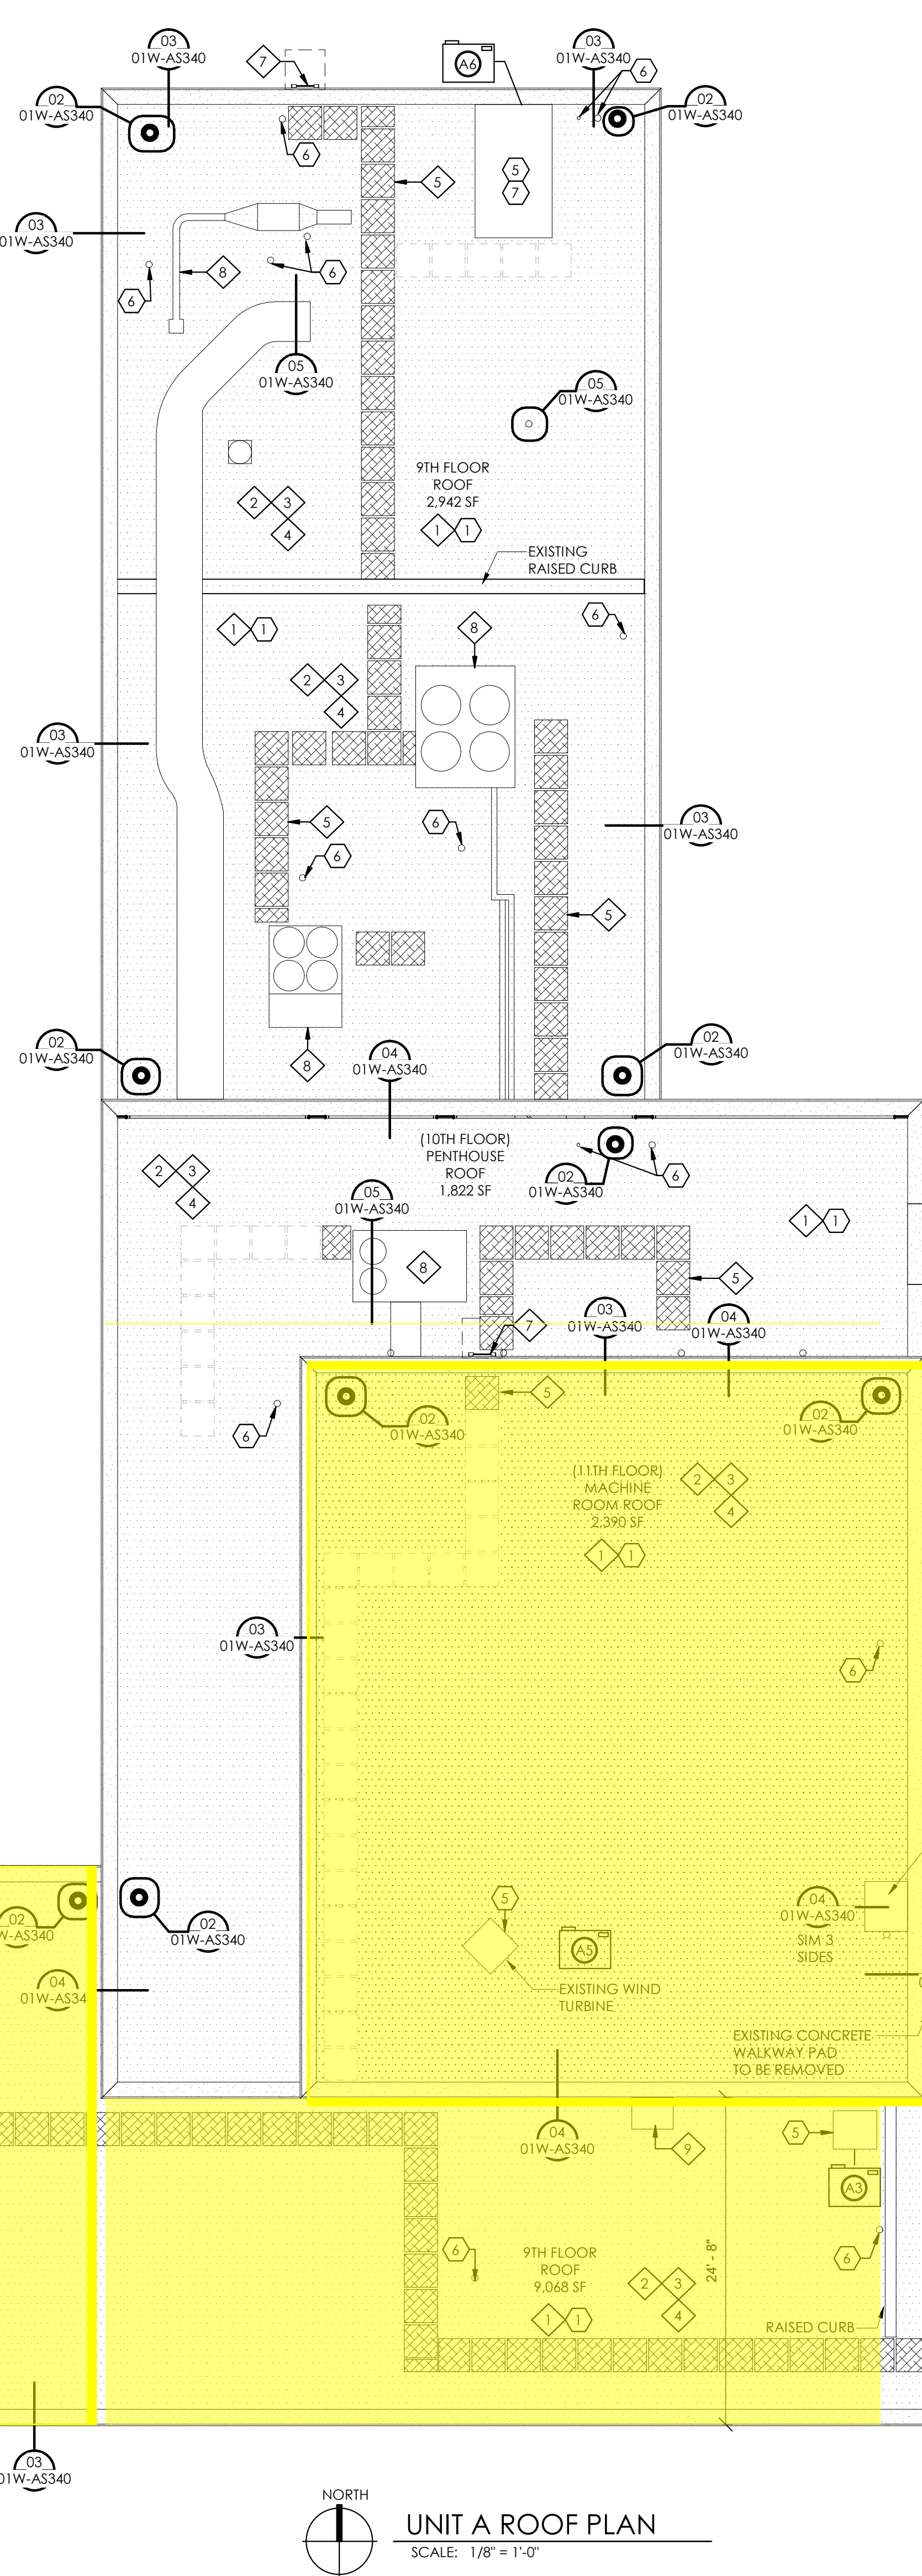

ROOF PLAN KEYNOTES	
1 NEW (LOW SLOPE) EPDM ROOFING AND INSULATION ON EXISTING DECK. PONDING NOT ALLOWED @ ANY LOCATION. ALTERNATE 1: ADDITIONAL INSULATION AND EPDM OVER EXISTING INSULATION.	5 FURNISH AND INSTALL NEW ROOFING WALKWAY PADS IN AREAS SHOWN. PADS SHALL BE ADHERED TO THE ROOF. COLOR TO BE BLACK. SEE SPECIFICATION FOR FURTHER INFORMATION.
2 DESIGN/INSTALL NEW LIGHTNING PROTECTION SYSTEM AND INCLUDE ALL APPURTENANCES FOR A COMPLETE AND FUNCTIONAL SYSTEM. BOND MIPE EQUIPMENT NEAR LP DOWNSLEADS. CONTRACTOR IS RESPONSIBLE FOR PROVIDING CONTINUITY TESTING AS REQUIRED FOR CERTIFICATION OF THE SYSTEM (SEE DESIGN/BUILD PERFORMANCE SPECIFICATION - 26 41 00 FACILITY LIGHTNING PROTECTION).	6 CONTRACTOR SHALL RELOCATE ANY EXISTING EQUIPMENT DURING ROOF REPLACEMENT ACTIVITIES. RELOCATION PLAN SHALL BE APPROVED BY COR PRIOR TO WORK.
3 CLEAN AND PROVIDE PROTECTION OVER AFFECTED AREA OF EXISTING FLAT ROOF DURING CONSTRUCTION PERIOD.	7 EXISTING WALL ATTACHED ROOF LADDER TO REMAIN.
4 CONTRACTOR TO HAVE EXISTING FLAT ROOF CLOSELY INSPECTED BY A 3RD PARTY CERTIFIED ROOFING INSPECTOR FAMILIAR WITH THE EXISTING ROOF SYSTEM. MANUFACTURER. INSPECT THE ROOF DECK AFTER ROOF AND INSULATION SYSTEM DEMO AND PRIOR TO INSTALLING NEW MEMBRANE SYSTEM. AS ROOFTOP UNITS AND LIGHTNING PROTECTION EQUIPMENT ARE RESET AND REINSTALLED. INSPECT TO VERIFY NO DAMAGE OCCURRED DURING THOSE INSTALLATIONS. MAKE ANY REPAIRS TO EXISTING ROOF FOUND DURING FINAL INSPECTION AT NO ADDITIONAL COST TO THE GOVERNMENT. CONTRACTOR SHALL NOTIFY COR 7 DAYS PRIOR TO INSPECTIONS AS THE COR MUST BE PRESENT.	8 EXISTING ROOFTOP EQUIPMENT TO REMAIN. EXTEND CURB HEIGHTS AS NEEDED TO MAINTAIN 8" CLEAR ABOVE ADJACENT ROOF PLANES. PATCH AND REPAIR ANY ADJACENT SURFACES AS NEEDED.
NOTE: ALL KEY NOTES FOR THE PROJECT ARE LISTED BUT DO NOT NECESSARILY APPLY TO EVERY PLAN OR ELEVATION. REFER TO DRAWINGS FOR APPLICABILITY.	

ROOF PLAN LEGEND	
	EXISTING ROOF DRAIN
	NEW MEMBRANE ROOFING
	EXISTING EXHAUST FAN (E.F.) OR RELIEF VENT (R.V.) IN ROOF AREA
	RUBBER WALKWAY TRAFFIC PAD
	EXISTING WALKWAY TRAFFIC PAD TO BE OMITTED
	PHOTO REFERENCE - SEE SHEET 01W-AS341

GENERAL NOTES - ROOF PLAN	
1. PRIOR TO COMMENCING EACH NEW PHASE OF WORK CONTRACTORS ARE TO VERIFY EXISTING FIELD CONDITIONS AND DIMENSIONS. INSPECT EXISTING WORK AREAS AND OBSERVE FOR ANY DAMAGE OR POTENTIAL ADVERSE EFFECT OF NEW WORK ON STRUCTURAL INTEGRITY OF THE BUILDING. IMMEDIATELY NOTIFY THE COR OF ALL DISCREPANCIES OR CONCERNS A MINIMUM OF (10) TEN WORKING DAYS IN ADVANCE OF THE WORK.	10. CONTRACTOR SHALL NOT BLOCK AREAS OF INGRESS/EGRESS FOR VEHICLE TRAFFIC OR PATIENT/STAFF ACCESS DURING CONSTRUCTION ACTIVITIES. IF THIS CANNOT BE AVOIDED, WRITTEN PERMISSION MUST BE OBTAINED FROM THE COR PRIOR. PROVIDE TRAFFIC CONES OR BARRICADES AND/OR PROVIDE A PERSON AT THE SUBJECT AREA TO ALERT PEDESTRIANS DURING THE WORK.
2. CONTRACTOR SHALL PROVIDE ALL LABOR, MATERIALS, EQUIPMENT, TESTING & ALL APPURTENANCES TO COMPLETE THE PROJECT AND DELIVER A COMPLETE, FUNCTIONAL ROOF SYSTEM.	11. CONTRACTOR SHALL INSPECT ALL ROOF DECKS AND PARAPETS WHILE EXPOSED AFTER DEMOLITION OF ROOFING MATERIALS. ALL DAMAGED ROOF DECK AND PARAPET MATERIAL SHALL BE REMOVED AND REPLACED WITH NEW MATCHING ROOF DECK TO MATCH EXISTING. CONTRACTOR SHALL CARRY AN ALLOWANCE FOR 7% REPLACEMENT OF UNFORESEEN DAMAGED DECK (SEE ALLOWANCES).
3. PROVIDE MINIMUM 1/4" PER FOOT SLOPE AT ALL LOW-SLOPE ROOF AREAS. SLOPE TO DRAINS WITH A MINIMUM OF 3" INSULATION THICKNESS OF INSULATION AT THE LOWEST SUMP POINT, INCLUDING SCUPPERS.	12. UPON PROJECT COMPLETION, CONTRACTOR SHALL CONFIRM PROPER FUNCTION OF ROOF DRAINAGE SYSTEMS. CLEAR ANY CLOGS & REPLACE MISSING OR DAMAGED STRAINER BASKETS WITH NEW TO MATCH EXISTING QUALITY/FUNCTION AND WITH THE ABILITY TO SECURE/REMOVE FOR ROUTINE MAINTENANCE.
4. REPLACE FLASHING AROUND ALL ROOF PENETRATIONS INCLUDING BUT NOT LIMITED TO, STAND PIPES, PLUMBING VENTS, HVAC INTAKE/EXHAUST FANS, ETC.	13. CONTRACTOR IS RESPONSIBLE FOR HOSTING SUBMITTAL EXCHANGE IN ONLINE SUBMITTAL TRACKING PLATFORM.
5. ALL CONSTRUCTION AREAS ARE TO BE PROPERLY IDENTIFIED, CLEANED AND MAINTAINED BY THE CONTRACTOR ON A DAILY BASIS. NO CONSTRUCTION DEBRIS IS TO REMAIN ON SITE AT PROJECT COMPLETION.	
6. CONTRACTOR TO VERIFY CONSTRUCTION WASTE DUMPSTER LOCATIONS WITH THE COR PRIOR TO BEGINNING ANY DEMOLITION AT EACH BUILDING.	
7. ALL CONTRACTORS ARE TO PROTECT EXISTING EQUIPMENT, FINISHES AND BUILDING COMPONENTS FROM CONSTRUCTION ACTIVITIES.	
8. CONTRACTORS SHALL BE RESPONSIBLE FOR ANY/ALL DAMAGE CAUSED DURING CONSTRUCTION OPERATIONS INCLUDING BUT NOT LIMITED TO SIDEWALK, CURBS, BUILDINGS, IRRIGATION, PRIVATE PROPERTY, LAWN RESTORATION, ETC. THE CONTRACTOR SHALL NOTIFY THE COR IMMEDIATELY IF ANY DAMAGE OCCURS AS A RESULT OF WORK ACTIVITIES.	
9. CONTRACTOR IS TO TAKE PRECAUTIONARY MEASURES TO PROTECT ALL TURF, TREES AND PLANTS THAT ARE IN THE VICINITY OF CONSTRUCTION AREAS AND BE RESPONSIBLE TO REPAIR/REPLACE ANY DAMAGED VEGETATION AND/OR PERFORM ANY LAWN RESTORATION AS A RESULT.	

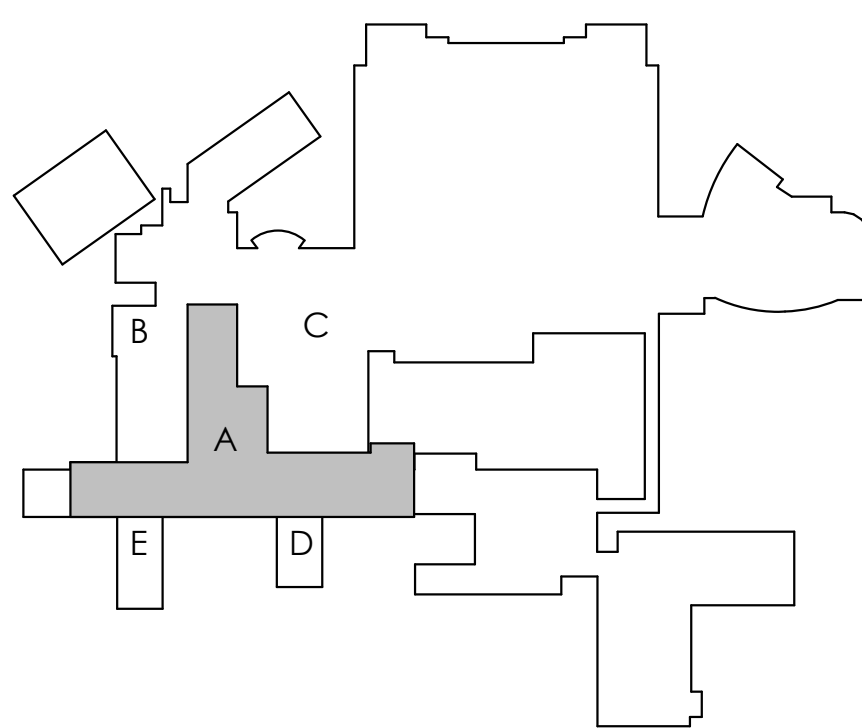

	</
--	--	----

1W - ROOF SLAB
956' - 8 3/4"

1W - MACHINE
ROOM SLAB
945' - 6"

1W - PENTHOUSE
931' - 0 3/4"

1W - 9TH FLOOR
920' - 0 3/4"

1W - 8TH FLOOR
908' - 7 1/4"

1W - 7TH FLOOR
896' - 8 1/4"

1W - 6TH FLOOR
885' - 8 1/4"

1W - 5TH FLOOR
873' - 9 1/4"

1W - 4TH FLOOR
861' - 2"

1W - 3RD FLOOR
850' - 2"

1W - 2ND FLOOR
839' - 2"

1W - 1ST FLOOR
827' - 3"

1W - BSMT
816' - 3"

1W - SUBBSMT
810' - 3"

UNIT B - 10TH FLOOR
PENTHOUSE ROOF

UNIT A - NORTH
7TH FLOOR ROOF

UNIT A - NORTH
8TH FLOOR ROOF

02 NORTH ELEVATION

01W-AS200 SCALE: 1/16" = 1'-0"

1W - ROOF SLAB
956' - 8 3/4"

1W - MACHINE
ROOM SLAB
945' - 6"

UNIT B - SOUTH 8TH
FLOOR ROOF

UNIT B - 10TH FLOOR
PENTHOUSE ROOF

UNIT B - SOUTH 8TH FLOOR ROOF

1W - PENTHOUSE
931' - 0 3/4"

1W - 9TH FLOOR
920' - 0 3/4"

1W - 8TH FLOOR
908' - 7 1/4"

1W - 7TH FLOOR
896' - 8 1/4"

1W - 6TH FLOOR
885' - 8 1/4"

1W - 5TH FLOOR
873' - 9 1/4"

1W - 4TH FLOOR
861' - 2"

1W - 3RD FLOOR
850' - 2"

1W - 2ND FLOOR
839' - 2"

1W - 1ST FLOOR
827' - 3"

1W - BSMT
816' - 3"

1W - SUBBSMT
810' - 3"

UNIT E - SOUTH ELECTRICAL ROOF

01 SOUTH ELEVATION

01W-AS200 SCALE: 1/16" = 1'-0"

CONSULTANT


ARCHITECT/ENGINEER OF RECORD

STAMP



400 E. Michigan Avenue, Suite B
Kalamazoo, MI 49007
P: 269.927.0144
www.7GenAE.com

1635 Prince Street
Alexandria, VA 22314
P: 202.617.8465
www.alliance.us.com

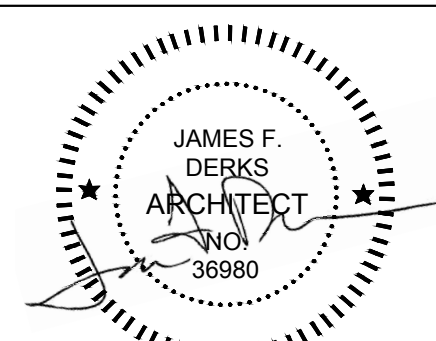

Office of
Construction
and Facilities
Management

VA U.S. Department
of Veterans Affairs

Drawing Title

EXTERIOR ELEVATIONS

Approved: PROJECT DIRECTOR

Phase

100% BID
DOCUMENTS

Sprinkler:

Project Title

ROOF REPLACEMENT

Location

ANN ARBOR VAMC

Issue Date

DECEMBER 1, 2023

Checked

JD

Drawn

GN

Project Number

220109

Building Number

1W

Drawing Number

01W-AS200

DWG. 05 OF 07

100% BID DOCUMENTS
Revisions:

12/01/23
Date:

A

B

C

D

E

F

A


B

C

D

E

F

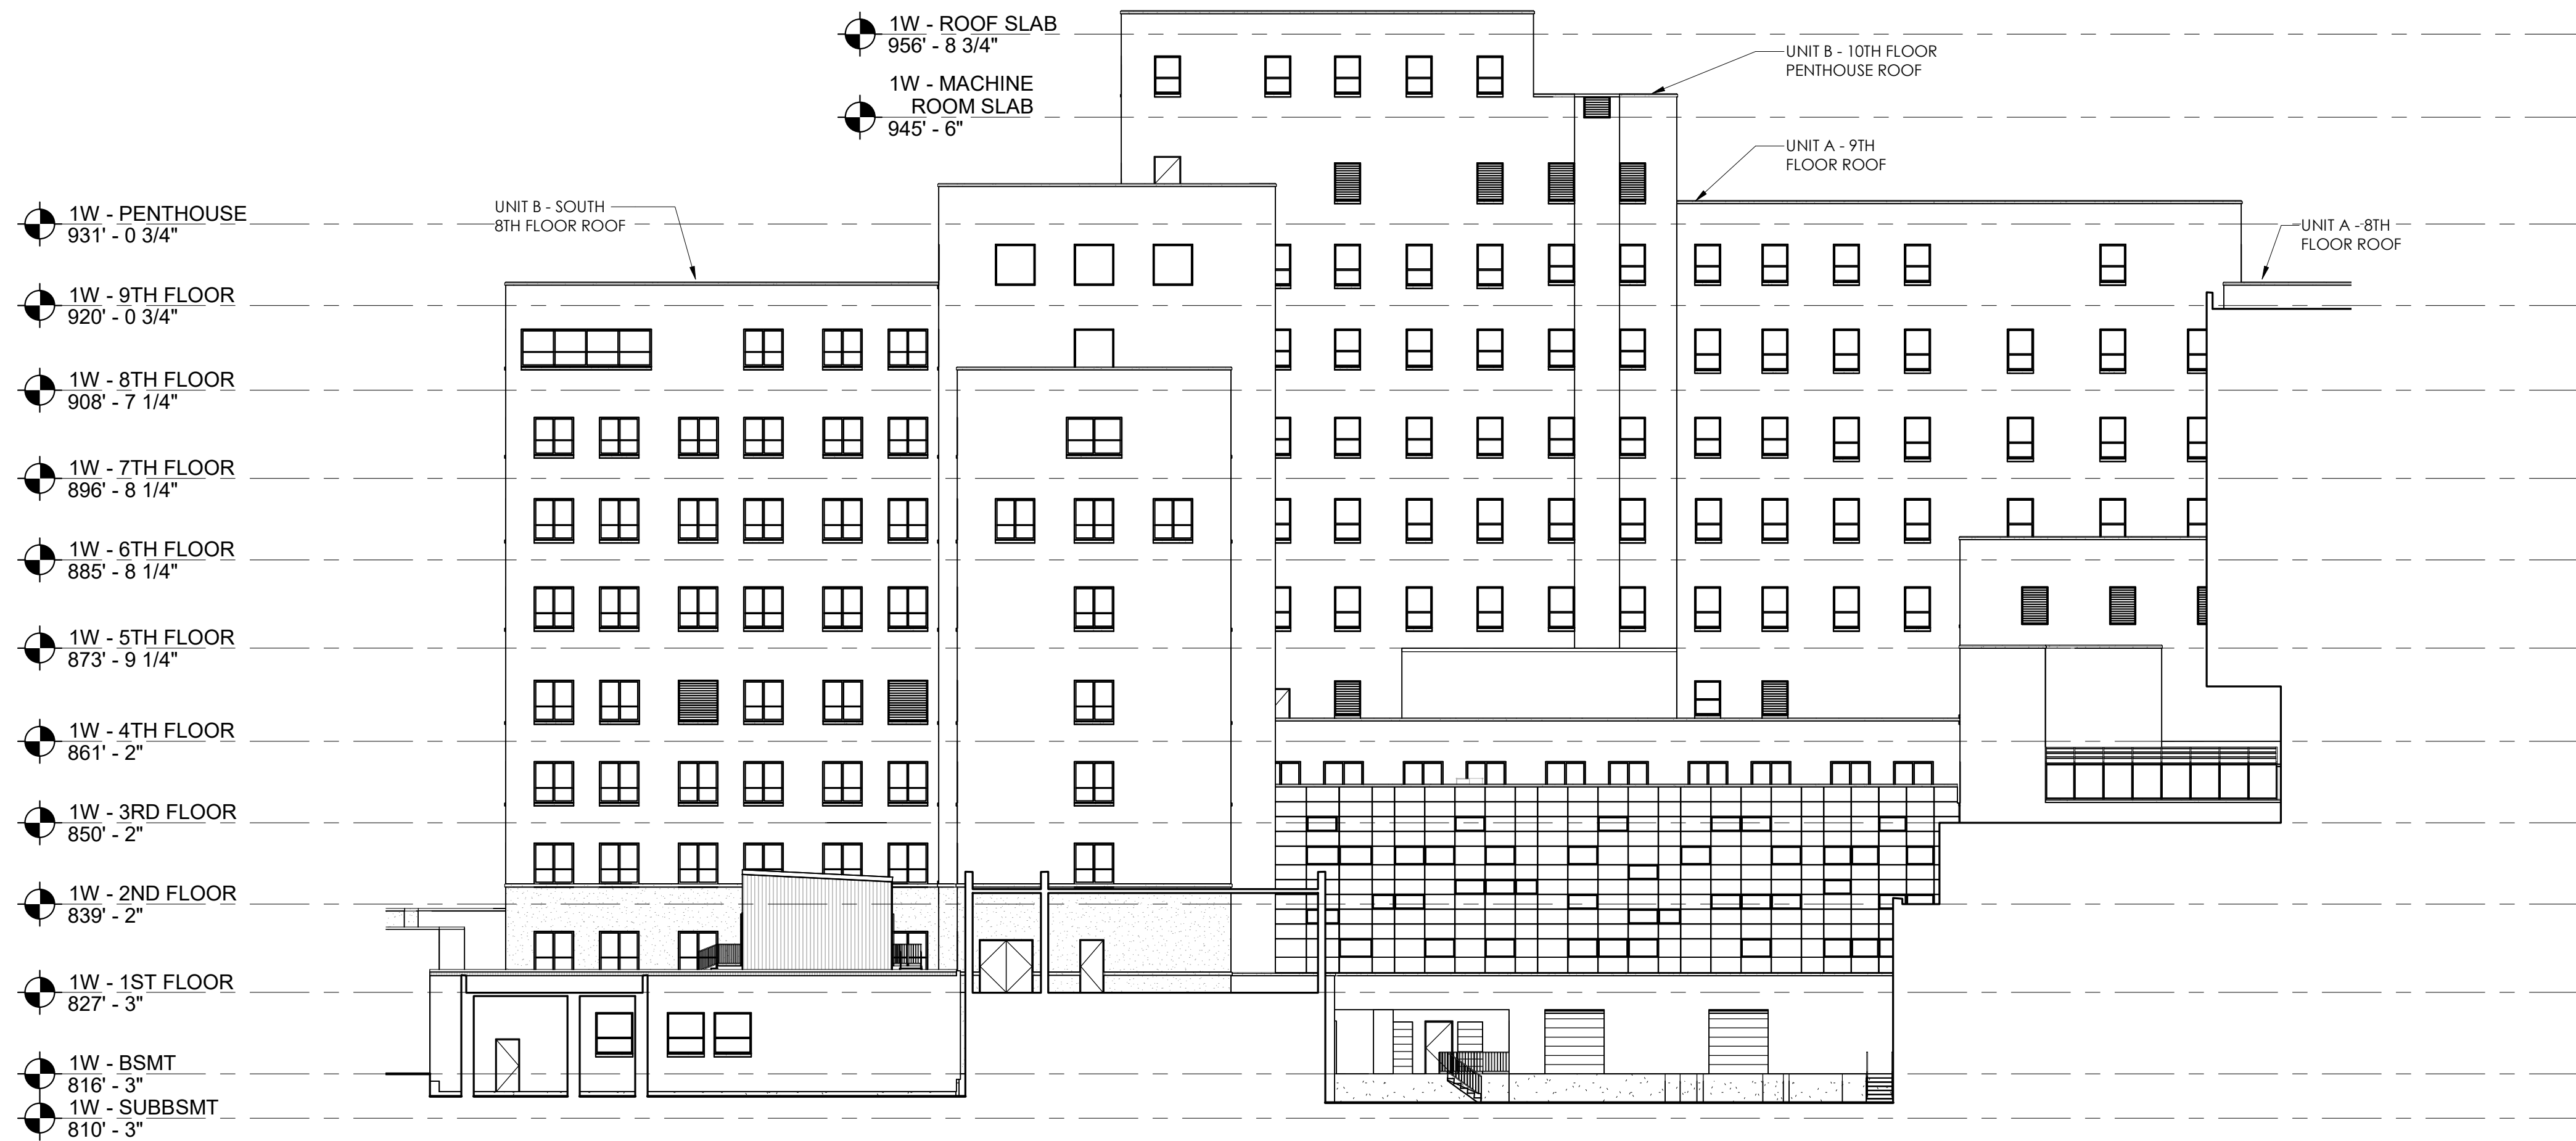

02 EAST ELEVATION
01W-AS201 SCALE: 1/16" = 1'-0"



01 WEST ELEVATION
01W-AS201 SCALE: 1/16" = 1'-0"

		CONSULTANT	ALLIANCE SEVEN GENERATIONS Offices • Consulting • General architectural • engineering Joint Venture 600 E. Michigan Avenue, Suite B Kalamazoo, MI 49007 P: 269.927.0144 www.7GenAE.com 1435 Prince Street Alexandria, VA 22314 P: 202.617.8465 www.alliance.us.com	JAMES F. DEBKS ARCHITECT 1636 36980	Office of Construction and Facilities Management VA U.S. Department of Veterans Affairs	Drawing Title	EXTERIOR ELEVATIONS	Phase	100% BID DOCUMENTS	Project Title	ROOF REPLACEMENT	Project Number	220109
												Building Number	
100% BID DOCUMENTS	12/01/23					Approved: PROJECT DIRECTOR	Sprinkler:	Location	ANN ARBOR VAMC	Drawing Number	01W-AS201		
Revisions:	Date:							Issue Date	DECEMBER 1, 2023	Checked	Checker		
								Drawn	Author		DWG. 06 OF 07		

